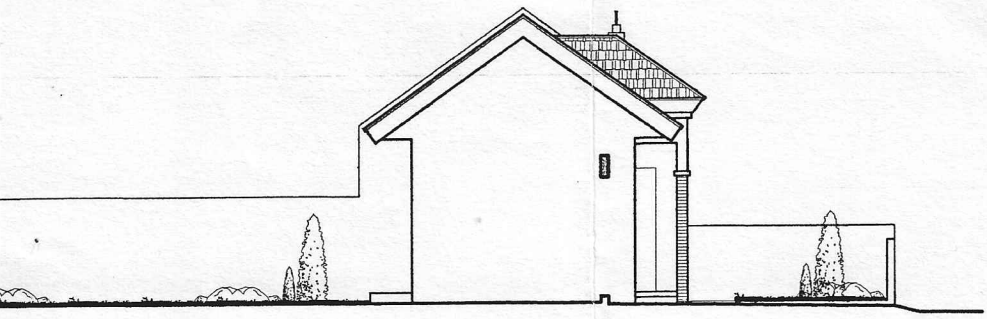

PING 3 / A-01

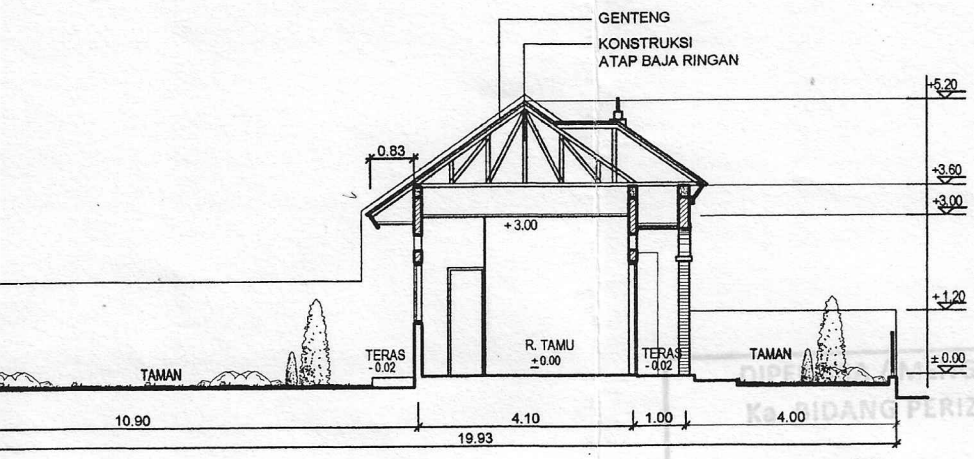

4 / A-01

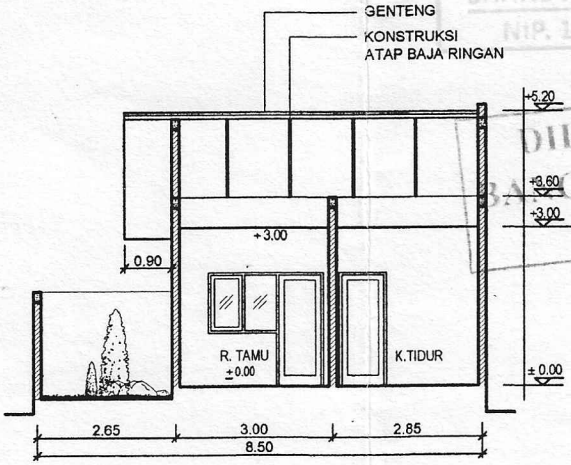

POTONGAN 5 / A-01
SKALA 1 : 100

CATATAN :

DEVELOPER :

PT. ARSY INDAH UTAMA
Jl. Wolter Monginsidi No. 112D, Jakarta

PROYEK :

PEMUKIMAN
SAWANGAN PERMAI

DIGAMBAR :
DIRENCANAKAN :
DIPERIKSA
DISETUJUI :
DISAHKAN :

DIPERINDAG KOTA TANGERANG SELATAN
Ka. BIDANG PERIZINAN I

SHANDY SYAMSURIZAL, S.Si., MP
NIP. 19771218 200112 1 002

GAMBAR :

DILARANG MERUBAH BANGUNAN DARI GAMBAR YANG DISETUJUI

DENAH , TAMPAK , POTONGAN
TYPE 27

NO. GAMBAR : A - 01
JUMLAH GAMBAR :
TANGGAL :
SKALA : 1 : 100

REVISI :